
*錠の有無 要確認
*取手・丁番 品番・取付位置 要確認
*染色色（色見本）・小口仕様 要確認

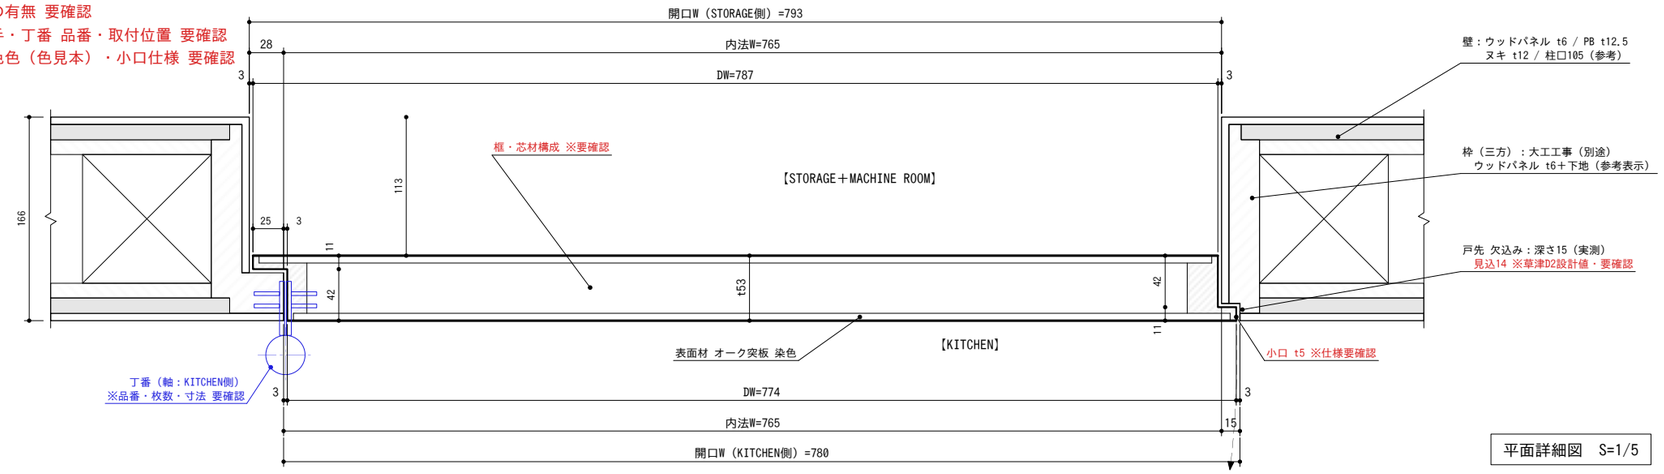


平面詳細図 S=1/5


記号	室 名	名 称	数量
1 / D2	KITCHEN／STORAGE	木製片開き戸	1

*仕様


扉寸法	KITCHEN面 W774×H1764	STORAGE面 W787×H1751
扉厚	t53（段欠き11＋本体42）	開き勝手：KITCHEN側へ開く
表面材	オーク突板 染色（両面）	染色色 ※色見本要確認
割付	各面4分割（巾は.0／.5）	K面193.5×4／S面196.5・197×2・196.5
小口	t5	※仕様要確認
芯材・框	※構成要確認	反り止め ※要否確認
枠	別途（大工工事）	ウッドパネル t6 仕上
丁番	軸：KITCHEN側	※品番・枚数要確認
取手	※種類要確認	※品番・取付高さ要確認
錠	※有無要確認	
戸当り	※要否確認	
備考	アンダーカット10	クリアランス 上・左右3

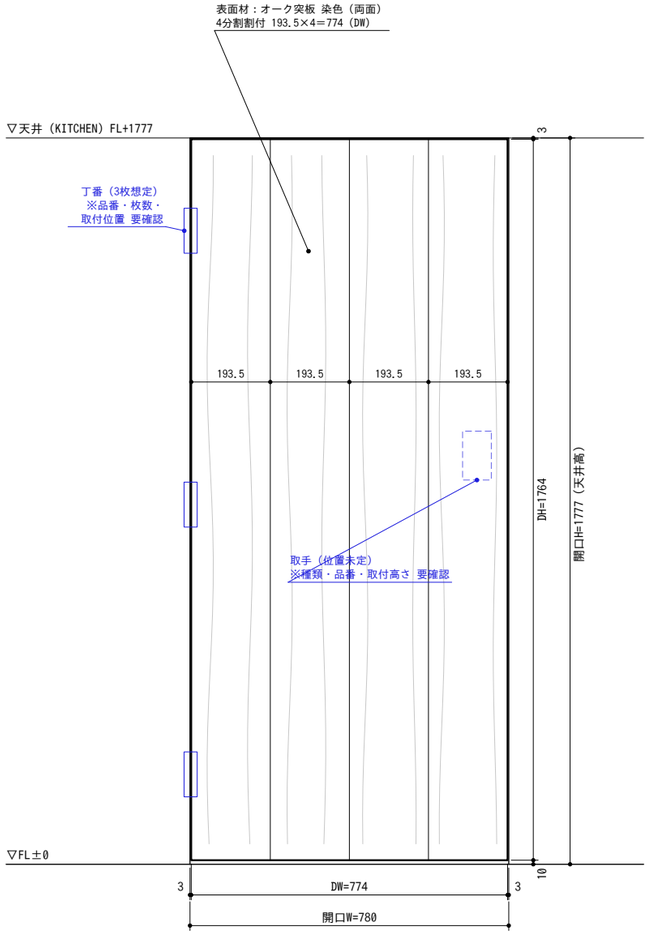


KITCHEN側 正面図 S=1/15

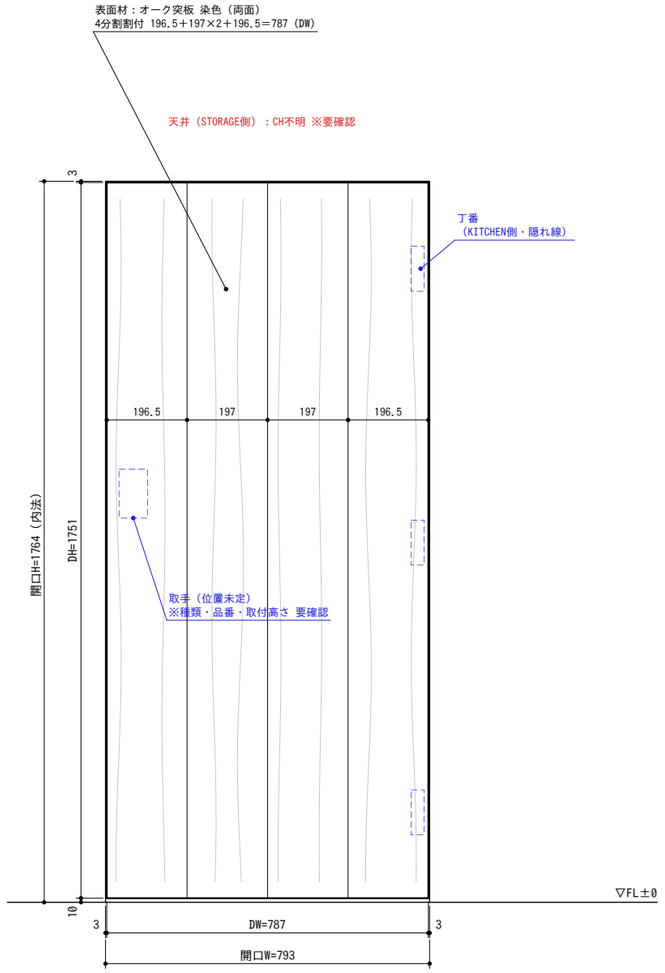


STORAGE側 正面図 S=1/15

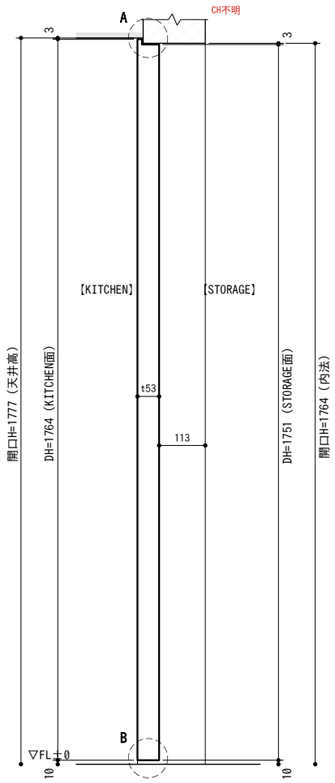

断面詳細図 S=1/15

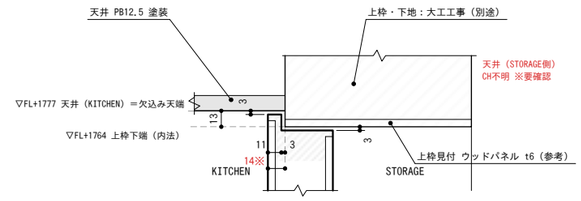

A：上部詳細 S=1/5

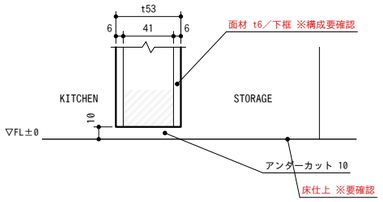

B：下部詳細 S=1/5

【特記】
・寸法単位：mm
・幅・高さは現場実測値（草津D2手書き 780／765／15、28、1777／1764、13）による
・扉厚53・面材t6・小口5・段欠き11・クリアランス3・アンダーカット10は草津D2（26.8.19）赤字寸法による
・欠込み見込14は草津D2設計値（実測なし）※要確認
・表面材：オーク突板 染色。各面を4分割割付し、1枚の巾は整数または.5とする（巾は扉見付寸法で割付）
・枠・下地・壁は大工工事（別途）。本図では参考表示
・丁番・取手の図示位置は参考（未確定）
・※印は未確定事項。製作前に要確認

会社名	工事名（PROJECT）	図面名（DRAWING TITLE）	改訂（REVISION）		縮尺（SCALE）	作図	図番（DRAWING NO.）
	KUSATSU Vacation rental PJ	D2 建具製作図 KITCHEN・STORAGE間 木製片開き戸	261016 図面作成		1/5・1/15（A3）		D2
					日付（DATE） 2026/10/16	検図	