
*錠の有無 要確認（トイレ用表示錠等）
*取手・丁番 品番・取付位置 要確認
*表面材・小口材 品番 要確認

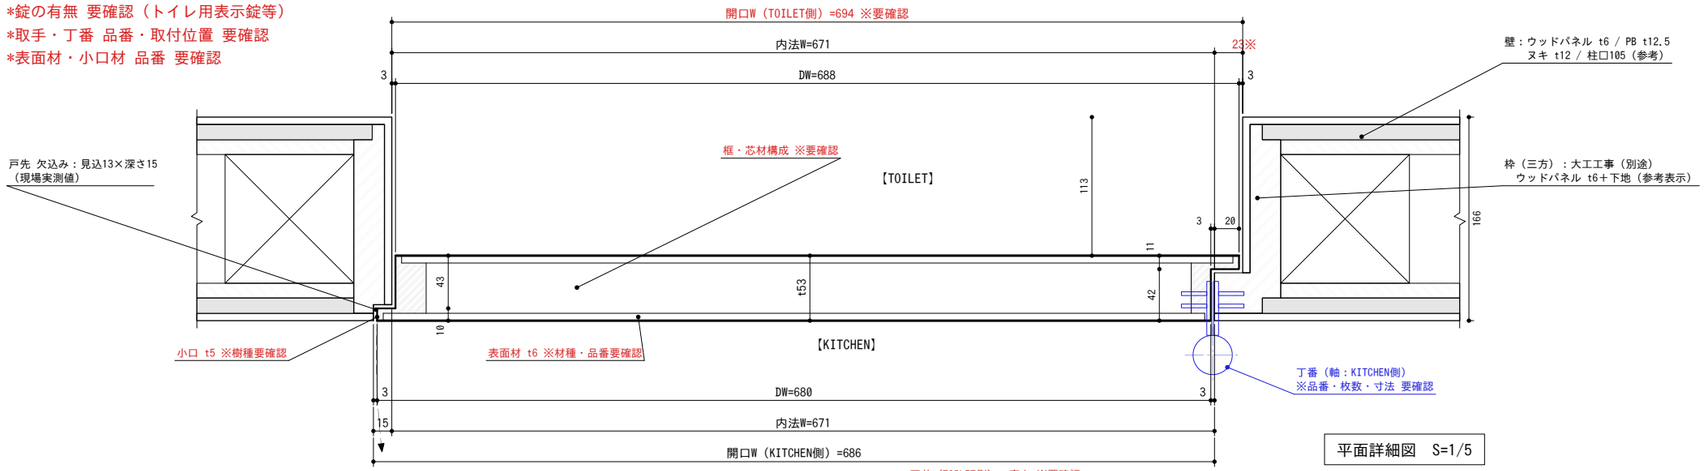


平面詳細図　S=1/5


記号	室　名	名　称	数量
1 / D1	KITCHEN／TOILET	木製片開き戸	1

*仕様


扉寸法	KITCHEN面 W680×H2367	TOILET面 W688×H2357
扉厚	t53（段欠き10＋本体43）	開き勝手：KITCHEN側へ開く
表面材	t6 両面	※材種・品番要確認
小口	t5	※樹種要確認
芯材・框	※構成要確認	反り止め ※要否確認
枠	別途（大工工事）	ウッドパネル t6 仕上
丁番	軸：KITCHEN側	※品番・枚数要確認
取手	※種類要確認	※品番・取付高さ要確認
錠	※有無要確認	（表示錠等）
戸当り	※要否確認	
備考	アンダーカット10	クリアランス 上・左右3

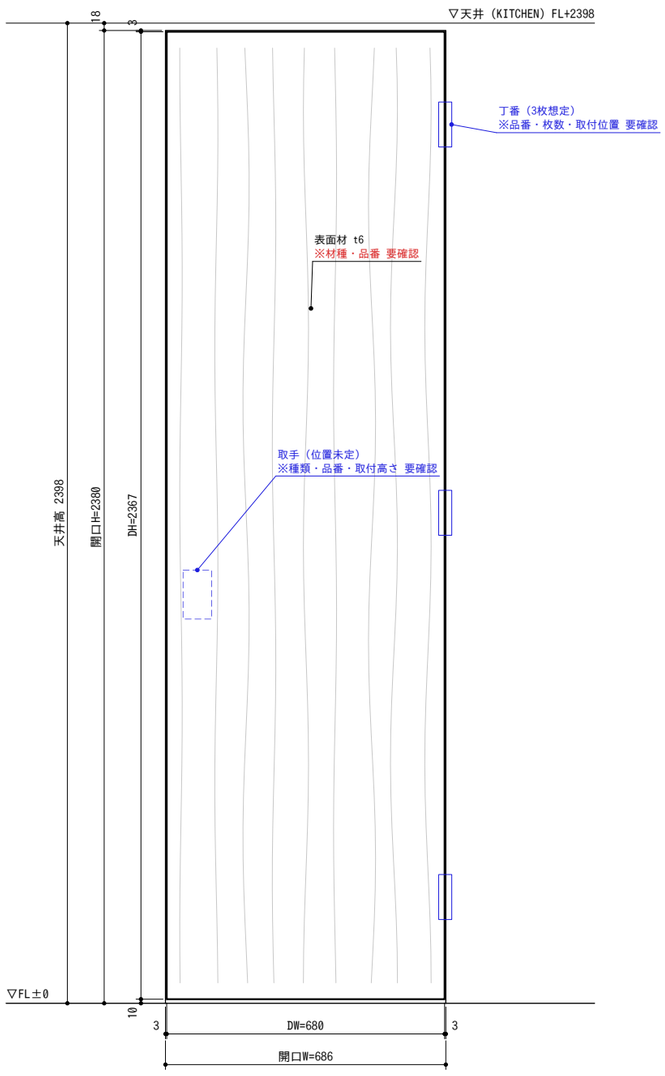


KITCHEN側 正面図　S=1/15

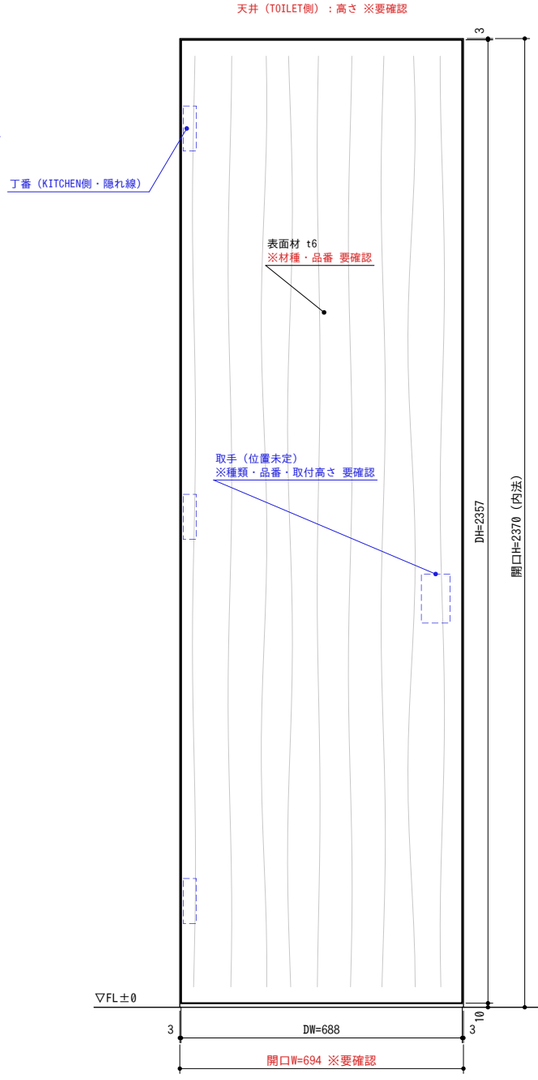


TOILET側 正面図　S=1/15

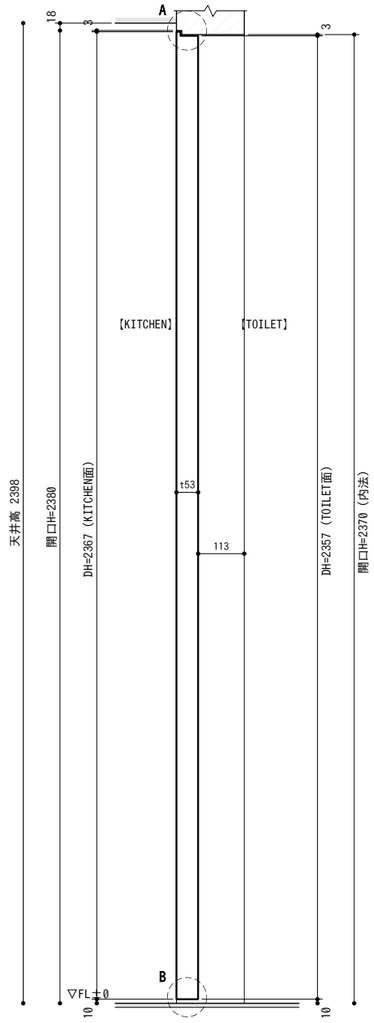

断面詳細図　S=1/15

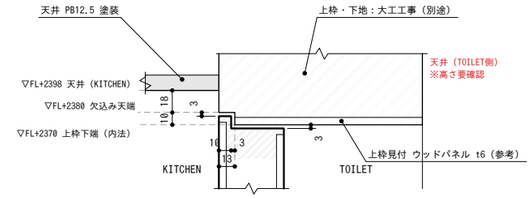

A：上部詳細　S=1/5

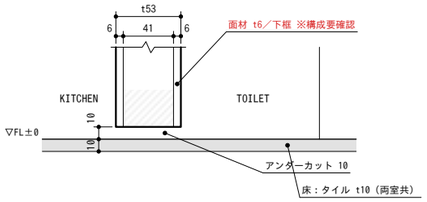

B：下部詳細　S=1/5

【特記】
・寸法単位：mm
・幅・高さは現場実測値（草津D1手書き 686／671／15、
2398／2380／2370、13）による
・扉厚53・面材t6・小口5・クリアランス3・アンダーカット10
は草津D1（26.8.19）赤字寸法による
・枠・下地・壁は大工工事（別途）。本図では参考表示
・吊元TOILET側の枠出23は草津D1設計値（実測なし）※要確認
・丁番・取手の図示位置は参考（未確定）
・※印は未確定事項。製作前に要確認

会社名	工事名（PROJECT）	図面名（DRAWING TITLE）	改訂（REVISION）		縮尺（SCALE）	作図	図番（DRAWING NO.）
	KUSATSU Vacation rental PJ	D1 建具製作図 KITCHEN・TOILET間 木製片開き戸	261016 図面作成		1/5・1/15（A3）		D1
					日付（DATE） 2026/10/16	検図	